


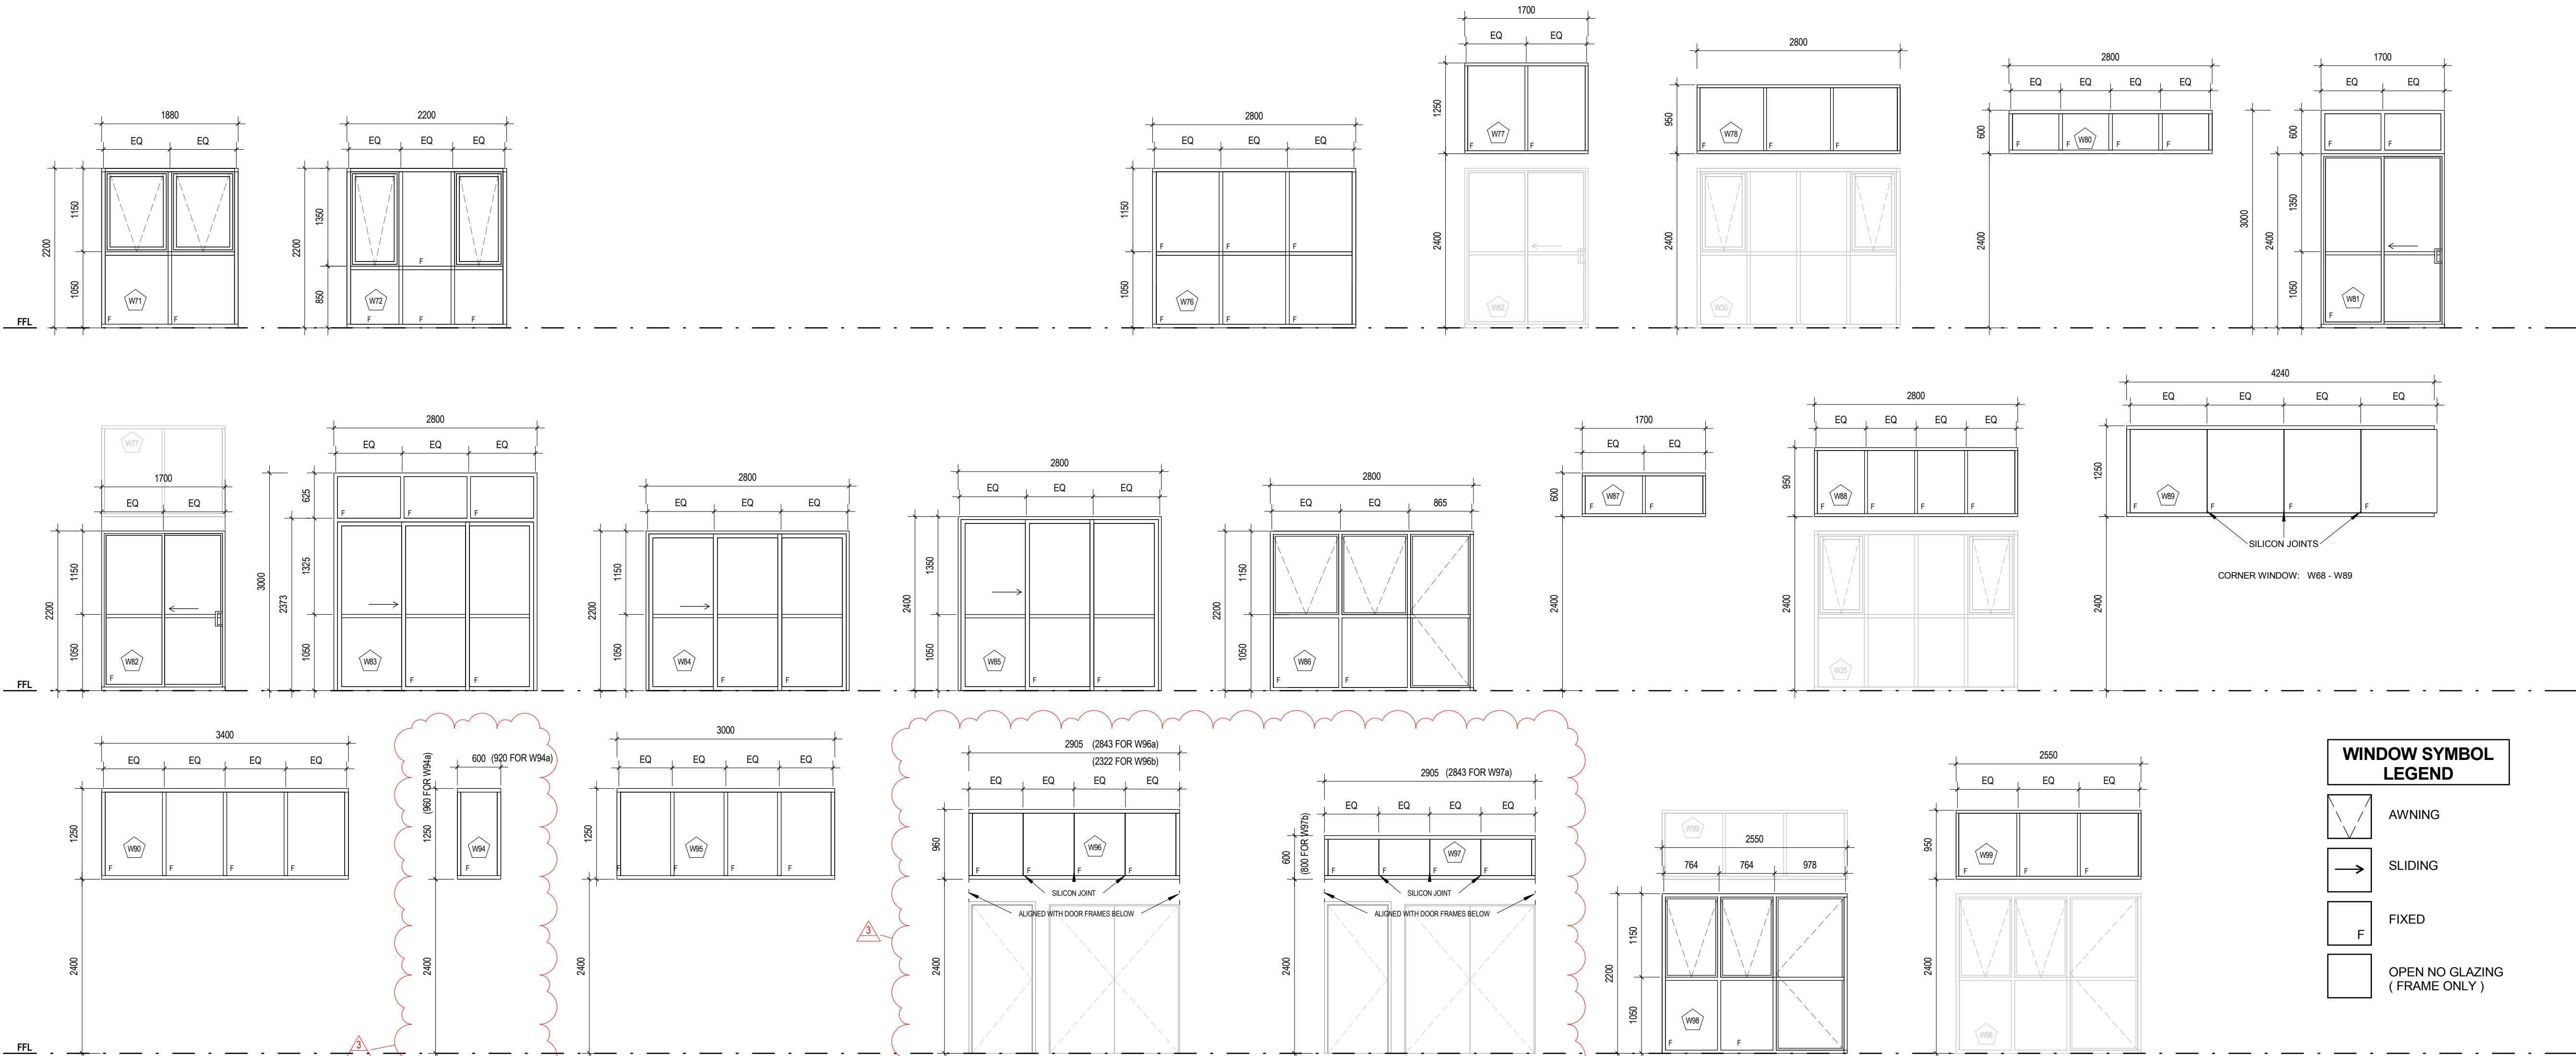

TYPE INFORMATION						
WINDOW	OPERATION	FRAME	GLAZING			
			HEIGHT	WIDTH	SILL HGT.	SPECIAL ITEMS
W71	Awning	Powder Coated Aluminium	To comply with the Dalgety Wool Store Risk Assessment, WGE Section J report and HSA Acoustic Report	0	0	0
W72	Awning	Powder Coated Aluminium	To comply with the Dalgety Wool Store Risk Assessment, WGE Section J report and HSA Acoustic Report	0	0	0
W73	Fixed	Powder Coated Aluminium	Internal Glazing	1250	3965	2400
W74	Fixed	Powder Coated Aluminium	Internal Glazing	1250	1588	2400
W76	Fixed	Powder Coated Aluminium	To comply with the Dalgety Wool Store Risk Assessment, WGE Section J report and HSA Acoustic Report	0	0	0
W77	Fixed	Powder Coated Aluminium	To comply with the Dalgety Wool Store Risk Assessment, WGE Section J report and HSA Acoustic Report	1250	1700	2400
W78	Fixed	Powder Coated Aluminium	To comply with the Dalgety Wool Store Risk Assessment, WGE Section J report and HSA Acoustic Report	950	2800	
W80	Fixed	Powder Coated Aluminium	To comply with the Dalgety Wool Store Risk Assessment, WGE Section J report and HSA Acoustic Report	600	2800	2400
W81	Sliding	Powder Coated Aluminium	To comply with the Dalgety Wool Store Risk Assessment, WGE Section J report and HSA Acoustic Report	3000	1700	0
W82	Sliding	Powder Coated Aluminium	To comply with the Dalgety Wool Store Risk Assessment, WGE Section J report and HSA Acoustic Report	2200	1700	0
W83	Sliding	Powder Coated Aluminium	To comply with the Dalgety Wool Store Risk Assessment, WGE Section J report and HSA Acoustic Report	3000	2800	0
W84	Sliding	Powder Coated Aluminium	To comply with the Dalgety Wool Store Risk Assessment, WGE Section J report and HSA Acoustic Report	2200	2800	0
W85	Sliding	Powder Coated Aluminium	To comply with the Dalgety Wool Store Risk Assessment, WGE Section J report and HSA Acoustic Report	2400	2800	0
W86	Swing / Awning Combination	Powder Coated Aluminium	To comply with the Dalgety Wool Store Risk Assessment, WGE Section J report and HSA Acoustic Report	2200	2800	0
W87	Fixed	Powder Coated Aluminium	To comply with the Dalgety Wool Store Risk Assessment, WGE Section J report and HSA Acoustic Report	600	1700	2400
W88	Fixed	Powder Coated Aluminium	To comply with the Dalgety Wool Store Risk Assessment, WGE Section J report and HSA Acoustic Report	950	2800	2400
W89	Fixed	Powder Coated Aluminium	Internal Glazing	1250	4240	2400
W94	Fixed	Powder Coated Aluminium	Internal Glazing	1250	600	2400 630
W94a	Fixed	Powder Coated Aluminium	Internal Glazing	960	920	2400
W95	Fixed	Powder Coated Aluminium	Internal Glazing	1250	3000	2400
W96	Fixed	Powder Coated Aluminium	Internal Glazing	960	2905	2400
W96a	Fixed	Powder Coated Aluminium	Internal Glazing	960	2843	2400
W96b	Fixed	Powder Coated Aluminium	Internal Glazing	960	2322	2400
W97	Fixed	Powder Coated Aluminium	Internal Glazing	600	2905	2400
W97a	Fixed	Powder Coated Aluminium	Internal Glazing	600	2843	2400
W97b	Fixed	Powder Coated Aluminium	Internal Glazing	800	2905	2400
W98	Swing / Awning Combination	Powder Coated Aluminium	To comply with the Dalgety Wool Store Risk Assessment, WGE Section J report and HSA Acoustic Report	2200	2550	0
W99	Fixed	Powder Coated Aluminium	To comply with the Dalgety Wool Store Risk Assessment, WGE Section J report and HSA Acoustic Report	950	2550	2630

LEVEL	WINDOW NO.	SILL HEIGHT	LOCATION (APT NO)	BLDG
-------	------------	-------------	-------------------	------

W71	LEVEL 4	182.2	0	182 (Mezz)	A
W71: 2	LEVEL 4	183.2	0	183 (Mezz)	A

W72	LEVEL 4	174.4	0	174 (Mezz)	A
W72: 1	LEVEL 4	174.4	0	174 (Mezz)	A

W73	LEVEL 2	30.6	2400	30	C
W73: 1	LEVEL 2	30.6	2400	30	C

W74	LEVEL 2	30.9	2400	30	C
W74: 1	LEVEL 2	30.9	2400	30	C

W76	LEVEL 4	113.2	0	113	B
W76: 1	LEVEL 4	113.2	0	113	B

LEVEL 1	67.4	2400	67	B
LEVEL 1	68.4	2400	68	B
LEVEL 1	69.4	2400	69	B
LEVEL 1	70.4	2400	70	B
LEVEL 1	71.4	2400	71	B
LEVEL 1	72.4	2400	72	B
LEVEL 1	73.4	2400	73	B
LEVEL 1	74.4	2400	74	B
LEVEL 1	75.4	2400	75	B
LEVEL 1	76.4	2400	76	B
LEVEL 1	77.4	2400	77	B
LEVEL 1	78.4	2400	78	B
LEVEL 1	79.4	2400	79	B
LEVEL 1	80.4	2400	80	B
LEVEL 1	81.4	2400	81	B
LEVEL 1	82.4	2400	82	B
LEVEL 2	83.3	2400	85	B
LEVEL 2	85.3	2400	86	B
LEVEL 2	87.3	2400	87	B
LEVEL 2	88.3	2400	88	B
LEVEL 2	89.4	2400	89	B
LEVEL 2	90.4	2400	90	B
LEVEL 2	91.3	2400	91	B
LEVEL 2	92.3	2400	92	B
LEVEL 2	93.3	2400	93	B
LEVEL 2	94.3	2400	94	B
LEVEL 2	96.4	2400	96	B
LEVEL 2	97.4	2400	97	B
LEVEL 2	98.4	2400	98	B
LEVEL 2	99.4	2400	99	B
LEVEL 2	100.4	2400	100	B
LEVEL 3	120.4	2400	120-Bic	B
LEVEL 1	141.3	2400	141-Bic	A
LEVEL 1	142.3	2400	142	A
LEVEL 1	143.3	2400	143-Bic	A
LEVEL 1	145.3	2400	144	A
LEVEL 1	145.3	2400	145	A
LEVEL 2	158.3	2400	158-Bic	A
LEVEL 2	159.3	2400	159-Bic	A
LEVEL 2	160.3	2400	160-Bic	A
LEVEL 3	162.3	2400	161-Bic	A
LEVEL 3	162.3	2400	162	A

W77: 36