
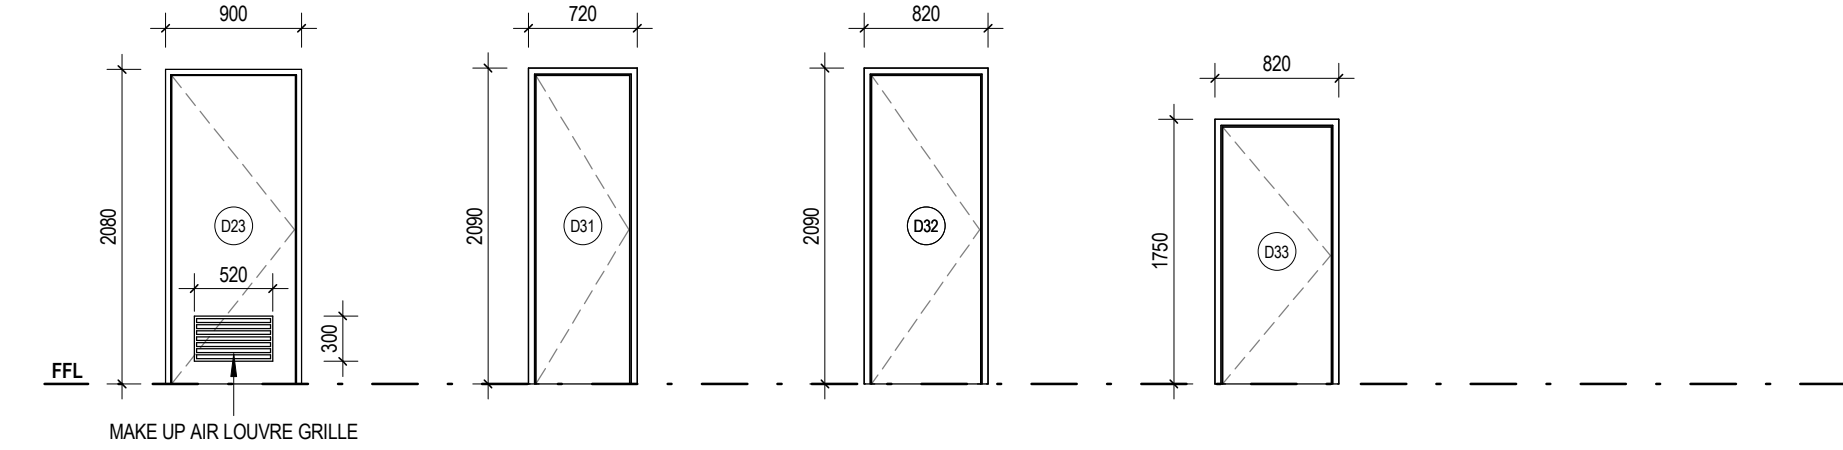
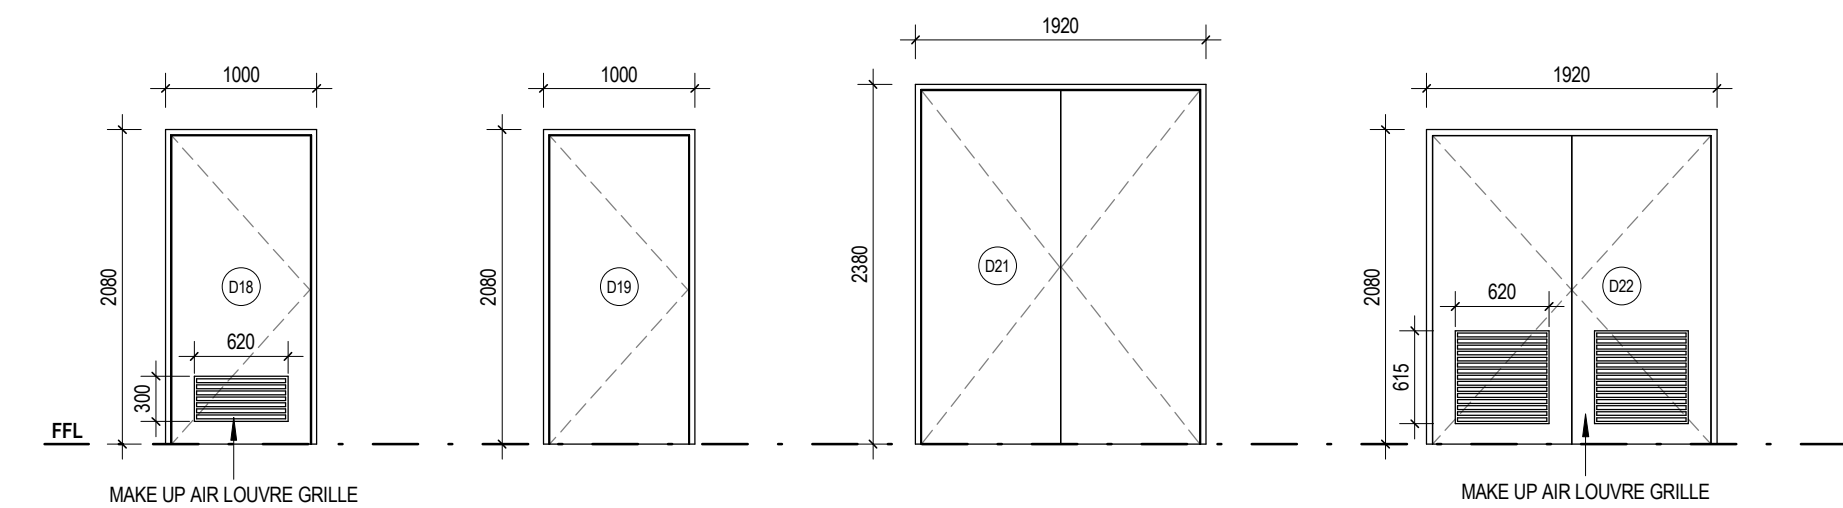
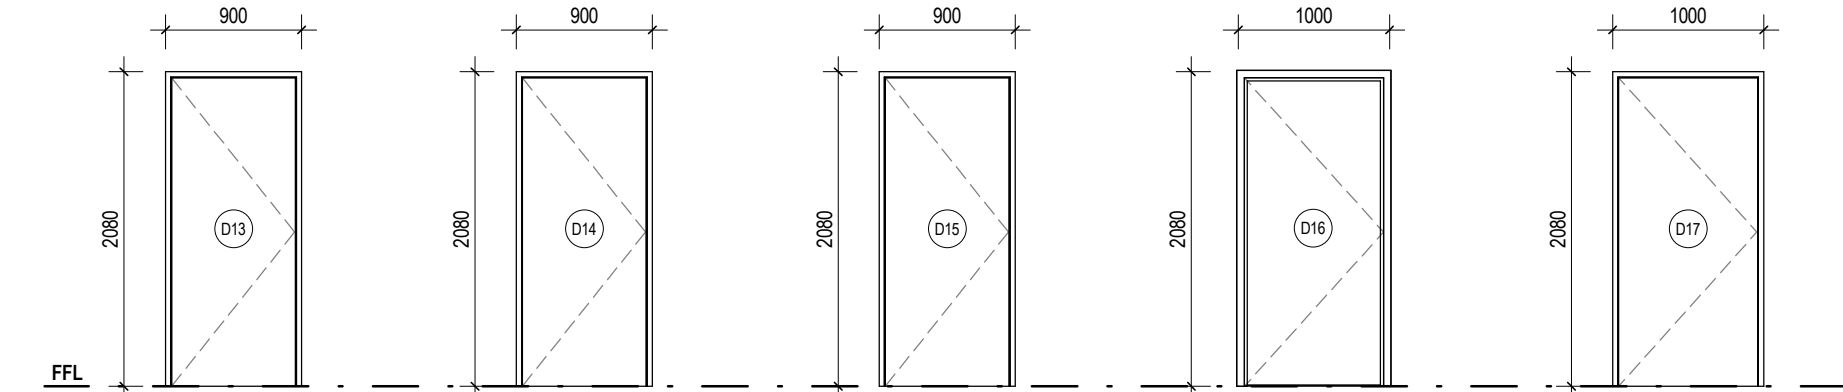


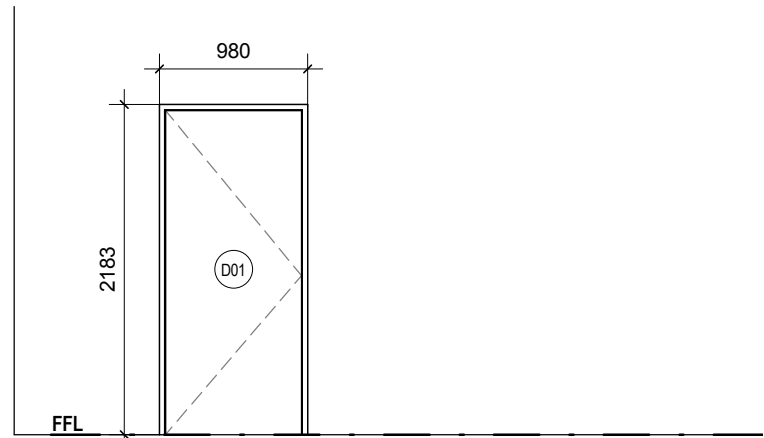

TYPE INFORMATION								
DOOR	Construction Type	WIDTH	HEIGHT	DESCRIPTION	FIRE DESIGNATION	FRAME TYPE	PANEL FINISH	SPECIAL ITEMS
D01	820 EXTERNAL FIRE DOOR	980	2183	FLUSH PANEL SOLID CORE DOOR	-/60/30	1.6MM GALVABOND EXTERNAL QUALITY	PAINT FINISH	SELF CLOSING DOOR-FREE HANDLE EGRESS
D13	820 EXTERNAL DOOR	900	2080	FLUSH PANEL SOLID CORE DOOR	-/60/30	1.6MM GALVABOND EXTERNAL QUALITY	PAINT FINISH	
D14	820 EXTERNAL FIRE DOOR	900	2080	FLUSH PANEL SOLID CORE DOOR	-/120/30	1.6MM GALVABOND EXTERNAL QUALITY	PAINT FINISH	SELF CLOSING DOOR - SMOKE SEALS -FREE HANDLE EGRESS
D15	820 EXTERNAL SMOKE DOOR	900	2080	FLUSH PANEL SOLID CORE DOOR	SMOKE SEALS	1.6MM GALVABOND EXTERNAL QUALITY	PAINT FINISH	SELF CLOSING DOOR - SMOKE SEALS
D16	920 INTERNAL FIRE DOOR	1000	2080	FLUSH PANEL HOLLOW CORE DOOR	-/120/30	1.2MM ZINC ANNEAL INTERNAL QUALITY	PAINT FINISH	SELF CLOSING DOOR
D17	920 EXTERNAL FIRE DOOR	1000	2080	FLUSH PANEL SOLID CORE DOOR	-/120/30	1.6MM GALVABOND EXTERNAL QUALITY	PAINT FINISH	SELF CLOSING DOOR - SMOKE SEALS
D18	920 EXTERNAL DOOR	1000	2080	FLUSH PANEL SOLID CORE DOOR		1.6MM GALVABOND EXTERNAL QUALITY	PAINT FINISH	MAKE-UP AIR LOUVRE GRILLE
D19	920 EXTERNAL DOOR	1000	2080	FLUSH PANEL SOLID CORE DOOR	NON-COMBUSTIBLE	1.6MM GALVABOND EXTERNAL QUALITY	PAINT FINISH	SELF CLOSING DOOR - SMOKE SEALS - NON-COMBUSTIBLE BACKING
D21	2 x 920 EXTERNAL FIRE DOORS	1920	2380	FLUSH PANEL SOLID CORE DOOR	-/120/30	1.6MM GALVABOND EXTERNAL QUALITY	PAINT FINISH	SELF CLOSING DOOR - SMOKE SEALS
D22	2 x 920 EXTERNAL FIRE DOORS	1840	2080	FLUSH PANEL SOLID CORE DOOR	-/120/30	1.6MM GALVABOND EXTERNAL QUALITY	PAINT FINISH	MAKE-UP AIR LOUVRE GRILLE
D23	820 EXTERNAL DOOR	900	2080	FLUSH PANEL SOLID CORE DOOR		1.6MM GALVABOND EXTERNAL QUALITY	PAINT FINISH	MAKE-UP AIR LOUVRE GRILLE
D31	620 INTERNAL DOOR	700	2080	FLUSH PANEL HOLLOW CORE DOOR		1.2MM ZINC ANNEAL HOLLOW CORE DOOR	PAINT FINISH	
D32	720 INTERNAL DOOR	800	2080	FLUSH PANEL HOLLOW CORE DOOR		1.2MM ZINC ANNEAL INTERNAL QUALITY	PAINT FINISH	
D33	720 INTERNAL DOOR	800	1740	FLUSH PANEL HOLLOW CORE DOOR		1.2MM ZINC ANNEAL INTERNAL QUALITY	PAINT FINISH	

LEVEL	DOOR NO.	LOCATION (APT NO)	BLDG
D01			
BASEMENT - LOWER	A.1		
BASEMENT - LOWER	A.2		
BASEMENT - UPPER	C.1		
BASEMENT - UPPER	C.2		
D01: 4			
D13			
LEVEL 3	#73		
BASEMENT - LOWER	A1.1		
BASEMENT - LOWER	A1.2		
BASEMENT - UPPER	A1.4		
LEVEL 1	A1.6	STAIR A1	A
LEVEL 2	A1.7	STAIR A1	A
LEVEL 3	A1.8	STAIR A1	A
BASEMENT - LOWER	A2.1		
BASEMENT - LOWER	A2.2		
BASEMENT - UPPER	A2.4	STAIR A2	A
LEVEL 1	A2.6	STAIR A2	A
LEVEL 2	A2.7	STAIR A2	A
LEVEL 3	A2.8	STAIR A2	A
BASEMENT - LOWER	A3.1	STAIR A3	A
BASEMENT - LOWER	A3.2	STAIR A3	A
LEVEL 1	A3.3		
LEVEL 2	A3.4	STAIR A3	A
LEVEL 3	A3.5	STAIR A3	A
BASEMENT - LOWER	B1.1		
BASEMENT - LOWER	B1.2		
BASEMENT - UPPER	B1.4	STAIR B1	B
LEVEL 1	B1.6	STAIR B1	B
LEVEL 2	B1.7	STAIR B1	B
LEVEL 3	B1.8	STAIR B1	B
BASEMENT - LOWER	B2.1		
BASEMENT - LOWER	B2.2		
BASEMENT - LOWER	B2.3		
BASEMENT - UPPER	B2.4		
BASEMENT - UPPER	B2.5		
LEVEL 1	B2.6	STAIR B2	B
LEVEL 2	B2.7		B
LEVEL 3	B2.8		B
BASEMENT - LOWER	B3.1		B
BASEMENT - UPPER	B3.3		
BASEMENT - UPPER	B3.4		
BASEMENT - UPPER	B3.5		
LEVEL 1	B3.7	STAIR B3	B
LEVEL 2	B3.8	STAIR B3	B
LEVEL 3	B3.9		
BASEMENT - LOWER	C1.1	STAIR C1	C
BASEMENT - UPPER	C1.3	STAIR C1	C
BASEMENT - UPPER	C1.4	STAIR C1	C
LEVEL 1	C1.6	STAIR C1	C
LEVEL 2	C1.7	STAIR C1	C
LEVEL 3	C1.8	STAIR C1	C
BASEMENT - LOWER	C2.1	SMOKE LOBBY C2	C
BASEMENT - UPPER	C2.3	STAIR C2	C
BASEMENT - UPPER	C2.4	FIRE EGR. CORRIDOR 1	C
BASEMENT - UPPER	C2.5	FIRE EGR. CORRIDOR 1	C
BASEMENT - UPPER	C2.7	FIRE EGR. CORRIDOR 1	C
LEVEL 1	C2.9	STAIR C2	C
LEVEL 2	C2.10	STAIR C2	C
LEVEL 3	C2.11	STAIR C2	C
BASEMENT - LOWER	C3.2	STAIR C3	C
BASEMENT - UPPER	C3.3	STAIR C3	C
BASEMENT - UPPER	C3.4	STAIR C3	C
LEVEL 1	C3.5	STAIR C3	C
LEVEL 2	C3.6	STAIR C3	C
LEVEL 3	C3.7	STAIR C3	C
BASEMENT - LOWER	CP.1	FIRE EGR. CORRIDOR 2	B
BASEMENT - UPPER	CP.22	CARPARK UPPER	Carpark
BASEMENT - UPPER	CP.25	FAN ROOM B	B
BASEMENT - UPPER	CP.27	CARPARK UPPER	Carpark
BASEMENT - UPPER	ST.128	ST. 128	Carpark
D13: 64			
D14			
SUBSTATION LEVEL	CP.18	SMSB	C
D14: 1			
D15			
BASEMENT - LOWER	A1.3		
BASEMENT - UPPER	A1.5		
BASEMENT - LOWER	A2.3		A
BASEMENT - UPPER	A2.5		
BASEMENT - LOWER	B1.3		B
BASEMENT - UPPER	B1.5		
BASEMENT - LOWER	B2.3	SMOKE LOBBY 1	C
BASEMENT - LOWER	B3.2		B
BASEMENT - UPPER	B3.6		
BASEMENT - LOWER	C1.2	SMOKE LOBBY C1	C
BASEMENT - UPPER	C1.5	CARPARK UPPER	Carpark
BASEMENT - LOWER	C2.2	SMOKE LOBBY C2	C
BASEMENT - UPPER	C2.6	CARPARK UPPER	Carpark
BASEMENT - UPPER	C2.8	SMOKE LOBBY C2	C
SUBSTATION LEVEL	C3.1	SMOKE LOBBY C3	C
BASEMENT - LOWER	CP.10	SMOKE LOBBY C7	C
BASEMENT - UPPER	CP.26	FAN ROOM C	C
D15: 17			
D16			
BASEMENT - LOWER	CP.11		
D16: 1			
D17			
SUBSTATION LEVEL	CP.14	SMSB	C
SUBSTATION LEVEL	CP.17	SMSB	C
D17: 2			

LEVEL	DOOR NO.	LOCATION (APT NO)	BLDG
D18			
BASEMENT - LOWER	CP.3	REFUSE STORE 1	Carpark
BASEMENT - LOWER	CP.4	REFUSE STORE 1	Carpark
BASEMENT - LOWER	CP.5	REFUSE STORE 2	Carpark
BASEMENT - LOWER	CP.6	REFUSE STORE 2	Carpark
BASEMENT - LOWER	CP.7	REFUSE STORE 3	Carpark
BASEMENT - LOWER	CP.8	REFUSE STORE 3	Carpark
D18: 6			
D19			
BASEMENT - UPPER	33.15	CARPARK UPPER	Carpark
BASEMENT - LOWER	CP.12	COMMS 1	C
D19: 2			
D21			
SUBSTATION LEVEL	CP.15	SUBSTATION	C
D21: 1			
D22			
BASEMENT - LOWER	CP.13	PUMP ROOM	C
D22: 1			
D23			
Cafe	A.4	CORRIDOR (CAFE)	
Cafe	A.5	CORRIDOR (CAFE)	
SUBSTATION LEVEL	CP.16	BM ROOM	C
BASEMENT - UPPER	CP.23	CARPARK UPPER	Carpark
D23: 4			
D31			
LEVEL 4	43.6	43 (Mezz)	C
LEVEL 4	55.10	55	C
LEVEL 4	56.10	56	C
LEVEL 4	57.10	57	C
LEVEL 4	58.10	58	C
LEVEL 4	59.10	59	C
LEVEL 4	60.10	60	C
LEVEL 4	61.10	61	C
LEVEL 4	62.10	62	C
LEVEL 4	63.10	63	C
LEVEL 4	64.10	64	C
LEVEL 4	65.10	65	C
LEVEL 3	103.2	103	B
LEVEL 3	104.2	104	B
LEVEL 3	105.2	105	B
LEVEL 3	106.2	106	B
LEVEL 3	107.2	107	B
LEVEL 3	108.2	108	B
LEVEL 3	109.2	109	B
LEVEL 3	110.2	110	B
LEVEL 3	111.2	111	B
LEVEL 3	112.2	112	B
LEVEL 3	113.2	113	B
LEVEL 3	114.2	114	B
LEVEL 3	115.2	115	B
LEVEL 3	116.2	116	B
LEVEL 3	117.2	117	B
LEVEL 3	118.2	118	B
LEVEL 3	119.2	119	B
LEVEL 3	120.2	120	B
Cafe	A.3	ST.	A
Cafe	A.6		
D31: 29			
D32			
LEVEL 1	1.3	1	C
LEVEL 1	2.4	2	C
LEVEL 1	3.4	3	C
LEVEL 1	4.4	4	C
LEVEL 1	5.4	5	C
LEVEL 1	6.4	6	C
LEVEL 1	7.4	7	C
LEVEL 1	8.4	8	C
LEVEL 1	9.3	9	C
LEVEL 1	10.2	10	C
LEVEL 1	11.3	11	C
LEVEL 1	12.2	12	C
LEVEL 1	13.2	13	C
LEVEL 1	13.10	13	C
LEVEL 1	14.2	14	C
LEVEL 1	14.10	14	C
LEVEL 1	15.2	15	C
LEVEL 1	15.10	15	C
LEVEL 1	16.2	16	C
LEVEL 1	16.10	16	C
LEVEL 1	17.2	17	C
LEVEL 1	17.10	17	C
LEVEL 1	18.2	18	C
LEVEL 1	18.10	18	C
LEVEL 1	19.2	19	C
LEVEL 1	19.10	19	C
LEVEL 1	20.2	20	C
LEVEL 1	20.10	20	C
LEVEL 1	21.2	21	C
LEVEL 1	21.7	21	C
LEVEL 2	22.4	22	C
LEVEL 2	23.4	23	C
LEVEL 2	24.4	24	C
LEVEL 2	25.4	25	C
LEVEL 2	26.4	26	C
LEVEL 2	27.4	27	C
LEVEL 2	28.4	28	C
LEVEL 2	29.4	29	C
LEVEL 2	30.4	30	C
LEVEL 2	31.2	31	C
LEVEL 2	32.2	32	C
LEVEL 2	32.10	32	C
LEVEL 2	33.5	33	C
LEVEL 2	33.9	33	C
LEVEL 2	34.2	34	C

LEVEL	DOOR NO.	LOCATION (APT NO)	BLDG
LEVEL 2			
LEVEL 2	34.10	34	C
LEVEL 2	35.2	35	C
LEVEL 2	35.10	35	C
LEVEL 2	36.2	36	C
LEVEL 2	36.10	36	C
LEVEL 2	37.2	37	C
LEVEL 2	37.10	37	C
LEVEL 2	38.2	38	C
LEVEL 2	38.10	38	C
LEVEL 2	39.2	39	C
LEVEL 2	39.10	39	C
LEVEL 2	40.2	40	C
LEVEL 2	40.10	40	C
LEVEL 2	41.2	41	C
LEVEL 2	41.10	41	C
LEVEL 2	42.2	42	C
LEVEL 2	42.10	42	C
LEVEL 3	43.3	43	C
LEVEL 4	43.7	43 (Mezz)	C
LEVEL 3	44.5	44	C
LEVEL 4	44.9	44 (Mezz)	C
LEVEL 3	45.5	45	C
LEVEL 4	45.9	45 (Mezz)	C
LEVEL 3	46.5	46	C
LEVEL 4	46.9	46 (Mezz)	C
LEVEL 3	47.5	47	C
LEVEL 4	47.9	47 (Mezz)	C
LEVEL 3	48.5	48	C
LEVEL 4	48.9	48 (Mezz)	C
LEVEL 3	49.5	49	C
LEVEL 4	49.9	49 (Mezz)	C
LEVEL 3	50.5	50	C
LEVEL 4	50.9	50 (Mezz)	C
LEVEL 3	51.2	51	C
LEVEL 3	52.4	52	C
LEVEL 4	52.8	52 (Mezz)	C
LEVEL 4	53.3	53 (Mezz)	C
LEVEL 4	54.4	54	C
LEVEL 3	55.5	55	C
LEVEL 4	55.9	55	C
LEVEL 3	56.5	56	C
LEVEL 4	56.9	56	C
LEVEL 3	57.5	57	C
LEVEL 4	57.9	57	C
LEVEL 3	58.5	58	C
LEVEL 4	58.9	58	C
LEVEL 3	59.5	59	C
LEVEL 4	59.9	59	C
LEVEL 3	60.5	60	C
LEVEL 4	60.9	60	C
LEVEL 3	61.5	61	C
LEVEL 4	61.9	61	C
LEVEL 3	62.5	62	C
LEVEL 4	62.9	62	C
LEVEL 3	63.5	63	C
LEVEL 4	63.9	63	C
LEVEL 3	64.5	64	C
LEVEL 4	64.9	64	C
LEVEL 3	65.5	65	C
LEVEL 4	65.9	65	C
D32: 105			
D33			
LEVEL 3	55.2	55	C
LEVEL 3	56.2	56	C
LEVEL 3	57.2	57	C
LEVEL 3	58.2	58	C
LEVEL 3	59.2	59	C
LEVEL 3	60.2	60	C
LEVEL 3	61.2	61	C
LEVEL 3	62.2	62	C
LEVEL 3	63.2	63	C
LEVEL 3	64.2	64	C
LEVEL 3	65.2	65	C
D33: 11			

- NOTES
- DO NOT SCALE FROM DRAWINGS VERIFY ALL DIMENSIONS ON SITE BEFORE COMMENCING WORK
 - COPY OR THE REPRODUCTION OF THIS DRAWING IS STRICTLY PROHIBITED WITHOUT THE CONSENT OF CAMERON CHISHOLM & NICOL (WA) PTY LTD.
 - REFER TO ARCHITECTURAL DRAWING SHEET A01:20 FOR GENERAL ARCHITECTURAL LEGENDS AND NOTES

04/09/2015	2	REVISED CONSTRUCTION ISSUE	DAW DB
28/08/2015	1		

Date	No.	Revision Description	Drawn
KEY PLAN			